外皮ZEH仕様,外周部構造用合板(妻壁部、及び母屋上げ部はﾀｲｶﾞｰEX防火妻壁※石膏ボード張上げ不要)

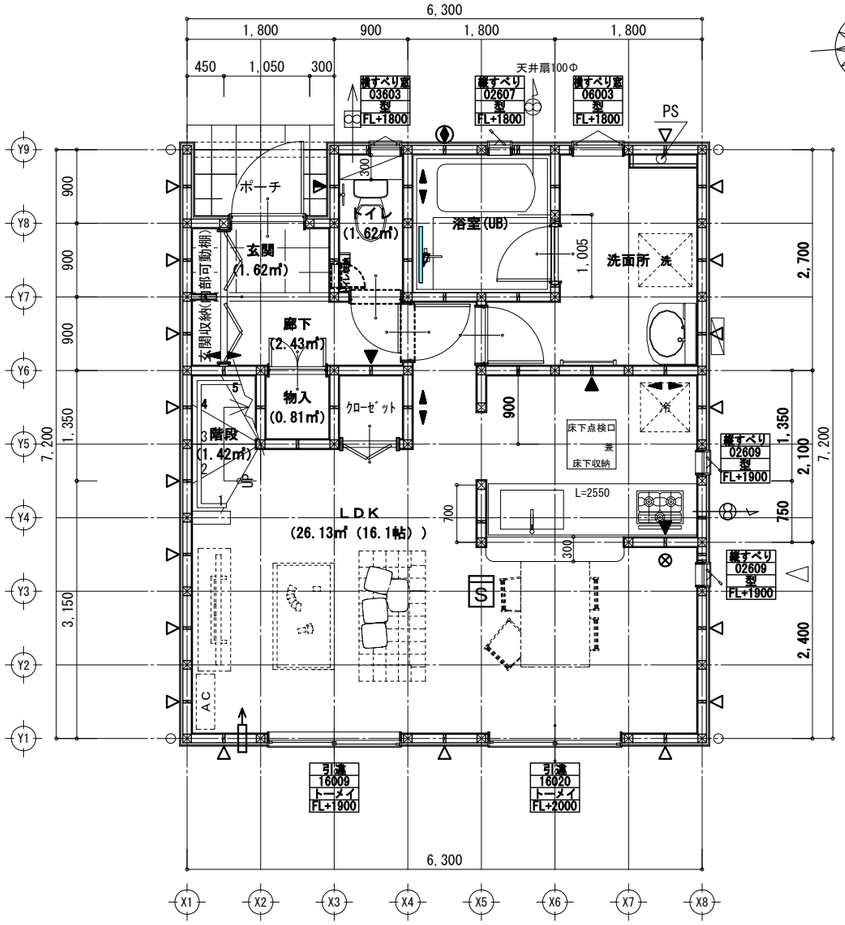

1階　平面詳細図 S:1/75

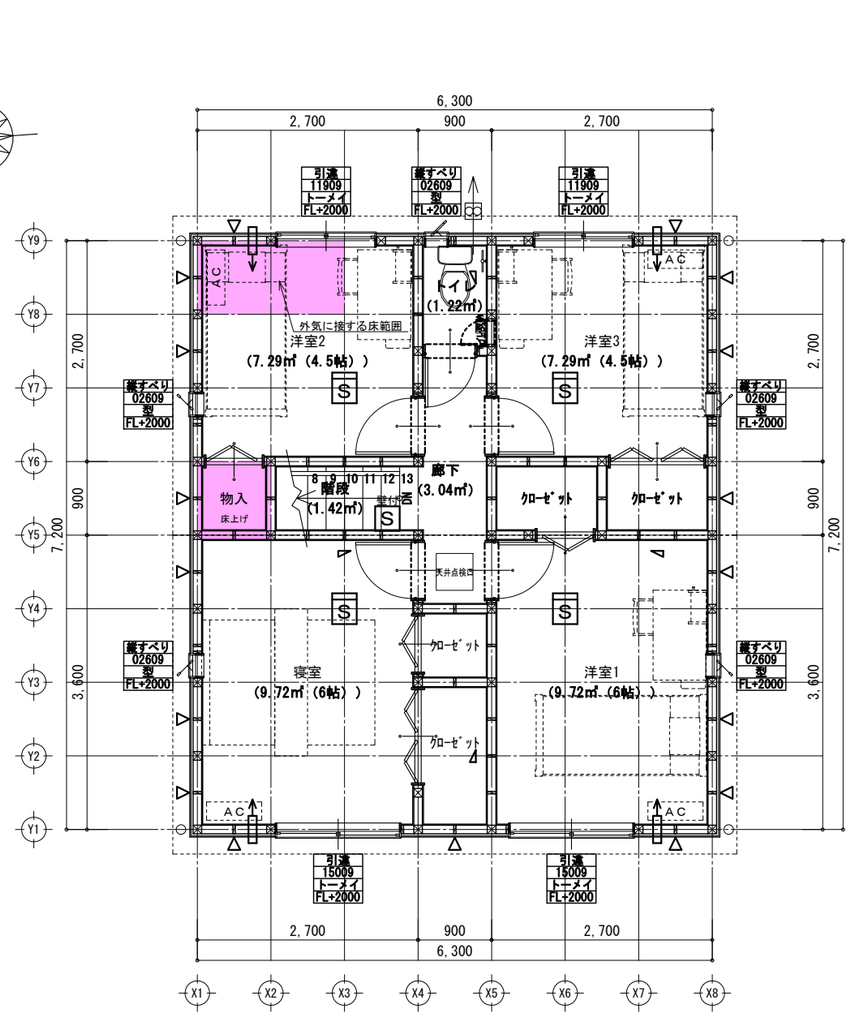

2階　平面詳細図 S:1/75

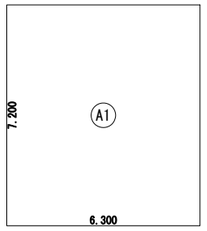

建築面積表			
	形状	計算式	面積
①	矩形	6,300×7,200	45,360000
		計(㎡)	計(坪)
合計		45.36	13.72

建築面積求積図 S:1/200

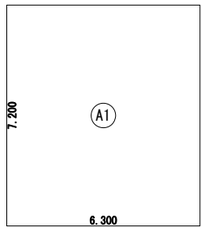

床面積表<2階>			
	形状	計算式	面積
①	矩形	6,300×7,200	45,360000
		計(㎡)	計(坪)
合計		45.36	13.72

2階　床面積求積図 S:1/200

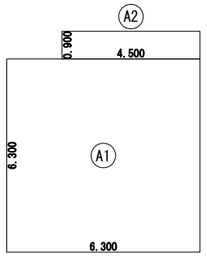

床面積表<1階>			
	形状	計算式	面積
①	矩形	6,300×6,300	39,690000
②	矩形	4,500×0,900	4,050000
		計(㎡)	計(坪)
合計		43.74	13.23

1階　床面積求積図 S:1/200

トータル面積表		(㎡)
敷地面積		117.62
建築面積		45.36
床面積	1階	43.74
	2階	45.36
延床面積		89.10
建蔽率	(45.36/117.62)×100	38.57%
容積率	(89.10/117.62)×100	75.76%

凡例

キッチン換気扇φ150(ﾀﾞｸﾄはｽﾊﾟｲﾗﾙとしﾌﾚｯｼｭﾀﾞｸﾄM（不燃MW-0241）、ﾌﾚｯｼｭﾍﾞｰ（性能評定番号E-065号）巻きとする）コンロと局レンジフード（不燃材）設置しシロッコファンで排気	タイガーEXハイパー(7)9.5mm（壁倍率2.7倍　FRM-0678）	ユニットバス換気扇100φ	タイガーEXハイパー(7)9.5mm（壁倍率2.2倍（床勝）FRM-0679）
柱　105×105	筋違（ダブル）90×45　令46条第4項表1（7）	構造用合板(7)9mm（壁倍率2.5倍）　告示1100号	石膏ボード12.5t（壁倍率1.1倍又は0.9倍※計算書参照）壁倍率1.1倍：FRM0274　壁倍率0.9倍：告示1100号
構造用合板(7)9mm（壁倍率3.7倍）　告示1100号	制震壁W900　令46条壁量用:FRM-0551　引抜用:FRM-0549	構造用合板(7)9mm（壁倍率3.7倍）+90×45（ｼﾝｸﾞﾙ）	シックハウス用給気口:FL+1,700　100φ
構造用合板(7)9mm（壁倍率3.3倍）　告示1100号	シックハウス用換気扇　100φ（スイッチには常時運転を指示する注意書きを貼る）	構造用合板(7)9mm（壁倍率3.3倍）+90×45（ｼﾝｸﾞﾙ）	アンダーカットドア(10mm以上)
筋違（シングル）90×45　令46条第4項表1（4）	壁付 S S 煙式警報器（型式適合検定合格品）天井付け壁面から600mm以上離す、壁付け天井から150から500以内に設置	給湯器	給気口　150φ

特記事項

階段寸法	蹴上230以下　踏面225（廻り部150）幅750以上 手摺の出　壁面より100以下
火気使用室内仕上(LDK)	天井：PB9.5mm下地ビニールクロス貼り 壁：PB12.5下地ビニールクロス貼り（準不燃：QM９４１０）
コンロ廻り仕上コンロから150mm以内の部分	下記の消防長が指定する有効な不燃材料とする PB(7)12.5mm※ｷｯﾁﾝﾊﾞﾈﾙ（不燃：NM-2183又はNM-0871）(7)3mm ｷｯﾁﾝ吊戸棚がある場合はｺﾝﾛから150mm離す
火気使用室換気計算(都市ガス・プロパン)	V＝30KQ　V＝30×0.93×9.9ｋｗ/ｈ＝277m/ｈ 277m/ｈ以上の換気能力の換気扇を設置する事
各居室間の床は段差の無い（5m/m以下）構造とする事。	
レースカーテンは別途とし、下地を設置することとする。	
耐力壁に使用するビスは、壁倍率1.1、@150以下 ビス：鞘カナイ　KT3928又はKT3932	
建築基準法施行令43条5項の通し柱に変わる柱の接合金物は、N値計算で算定した金物以上かつHD15KNとし1階と2階の柱どうしを緊結する事。	

耐力壁の取付く柱の仕口にあっては、告示1460号1項2号によるN値計算による。	
居室、天井裏等の部分、押入など建具等の表面材の使用建築材料については、規制対象外材料（Fｘｘｘｘ）のみを使用する。	
トイレ排水管には適切に通気管を設けること	
建築材料に石綿及びクロルピリホス（添加した建築材料を含む）を使用しないこと。	
○ 竪樋を示す ※現場、施工上により図面記載と相違する場合があります。	
⇨ 排水ドレンを示す ※現場、施工上により図面記載と相違する場合があります。	

備考

外壁を全て防火構造とするので、延焼ラインの記入を省略する	
防犯に関することの評価対象開口区分	a：住戸の出入口 b：比較的侵入容易な開口部 c：a．b以外の開口部

小屋裏換気計算

■棟換気金物必要数量算定(YY3003BS：1800一般地域)	45.36÷1600÷0.0396＝0.716　1本以上必要
軒裏換気口必要数量算定(SNV-70：W-900)	45.36÷900÷0.00747＝6.75本・・・7本以上必要

■ 性能表示住宅	□ オール電化
□ 外壁ALC	□ フラット35
□ 防火地域	□多雪区域（1m）
□ 準防火地域	□多雪区域（1.1m）
■ 防火指定無し	□多雪区域（1.2m）
□ 準耐火構造	□多雪区域（1.3m）

変更及特記事項

飯田グループホールディングス
株式会社アーネストワン
検査予約ﾒｰﾙｱﾄﾞﾚｽ：sekkei-kensayoyaku@arnest1.co.jp
株式会社アーネストワン福岡一級建築士事務所 福岡県知事登録　第1-60147号
福岡県知事登録　第32289号　二級建築士 若林　佑馬

原図	若林	熊本
	設計担当者	営業区分

工事名：大津町杉水第1(2棟)2号棟

26074000200

図面名：平面詳細図　AS北630720-3

縮尺　1/75